



ARCHITECTURAL PORTFOLIO

The author retains all copyrights in any text, graphic images and photos in this document. No part of it may be reproduced or transmitted in any form or by any means, electronic or mechanical including photocopying, recording or any information storage and retrieval system without permission in writing from the author.

© 2023




4-BEDROOM MAISONETTE- KISII COUNTY.

With four generously sized bedrooms, this home offers ample space for a growing family or those seeking room for a home office or guest accommodations.

Embraced by the scenic beauty of Kisii County, this maisonette is not just a home; it's a haven where comfort and sophistication converge.






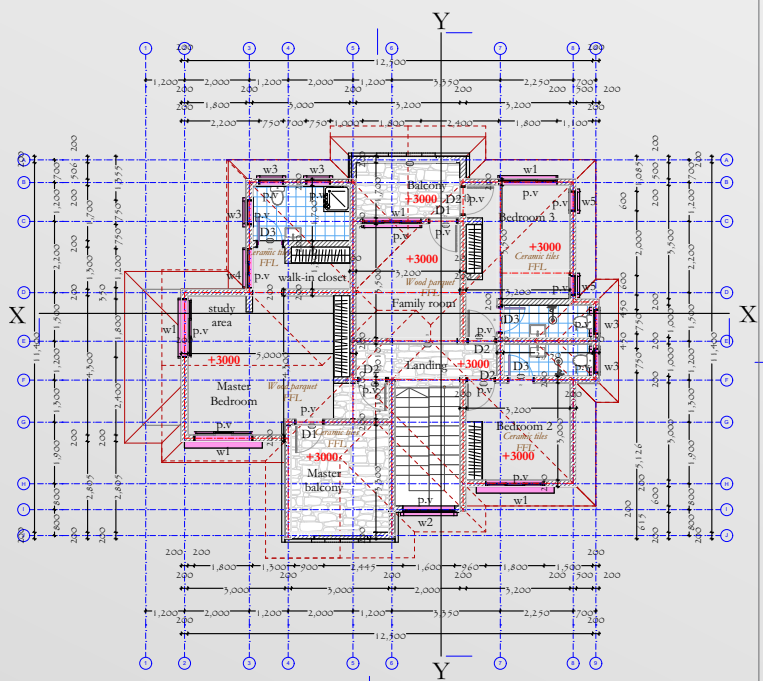



3-BEDROOM BUNGALOW



A charming 3-bedroom bungalow nestled in the serene locality of Joska, along Kangundo Road. This meticulously designed residence offers a perfect blend of modern comfort and tranquility. With its contemporary design, lush surroundings, and convenient location, this bungalow in Joska promises a delightful living experience for those seeking a peaceful retreat without compromising on style and functionality.

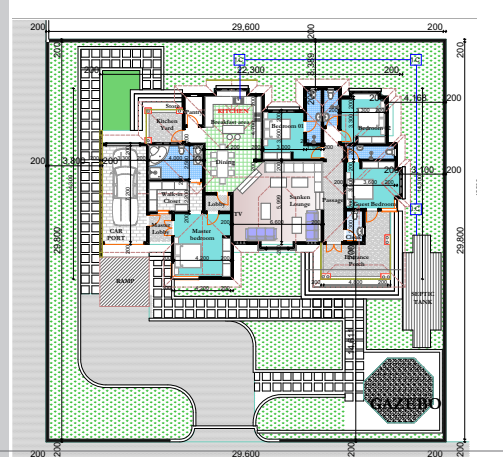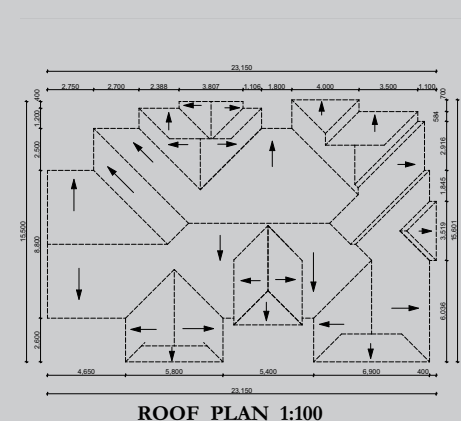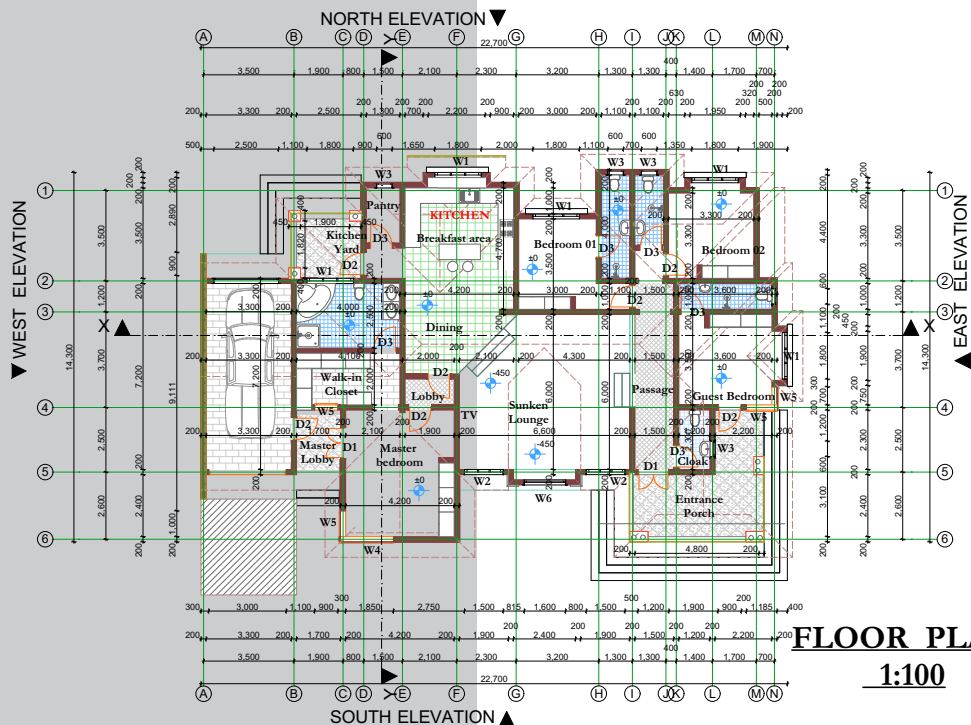



RUIRU APARTMENTS



This apartment complex embodies a seamless fusion of contemporary design and practical utility. The exterior facade is characterized by clean lines and expansive windows, facilitating abundant natural light to permeate the interiors. The one and two-bedroom units are thoughtfully configured to optimize spatial efficiency without compromising an open and inviting atmosphere.

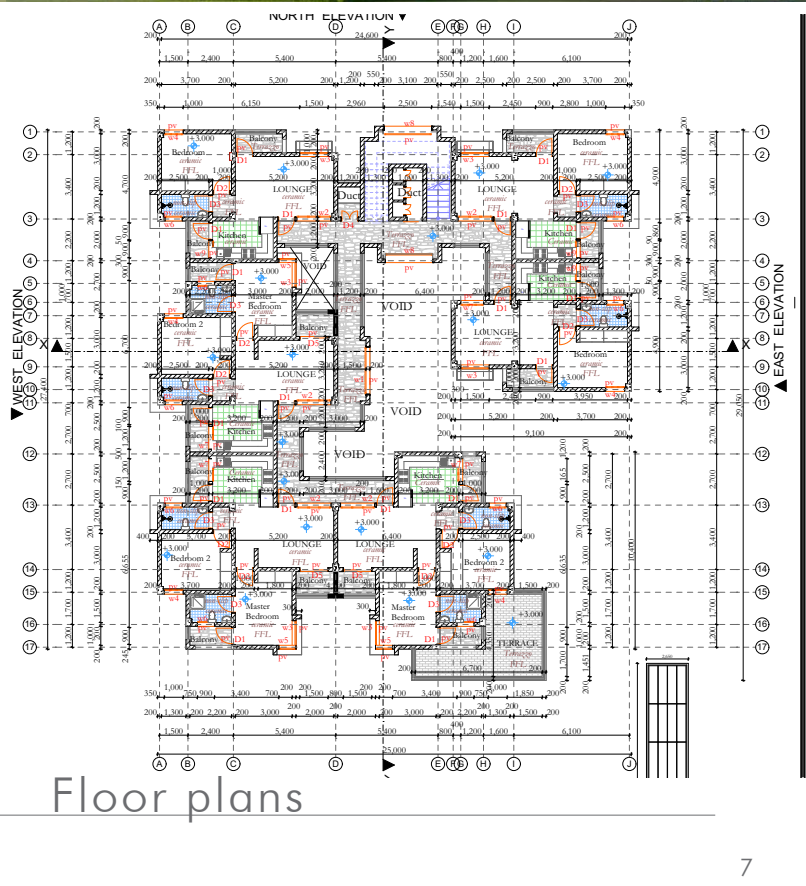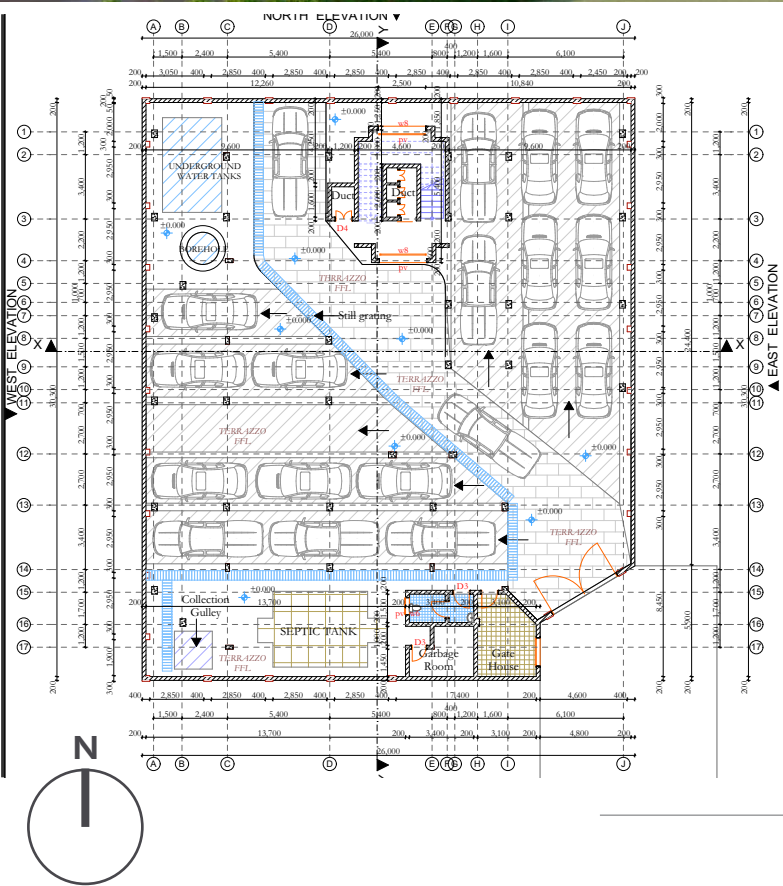


Floor plans

Private balconies or terraces offer residents a connection to the surrounding environment.

Additionally, a designated parking area ensures convenience for residents, aligning with the overall design principles of this urban residential enclave

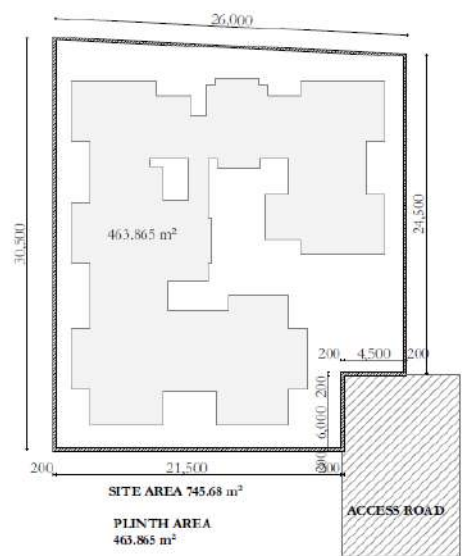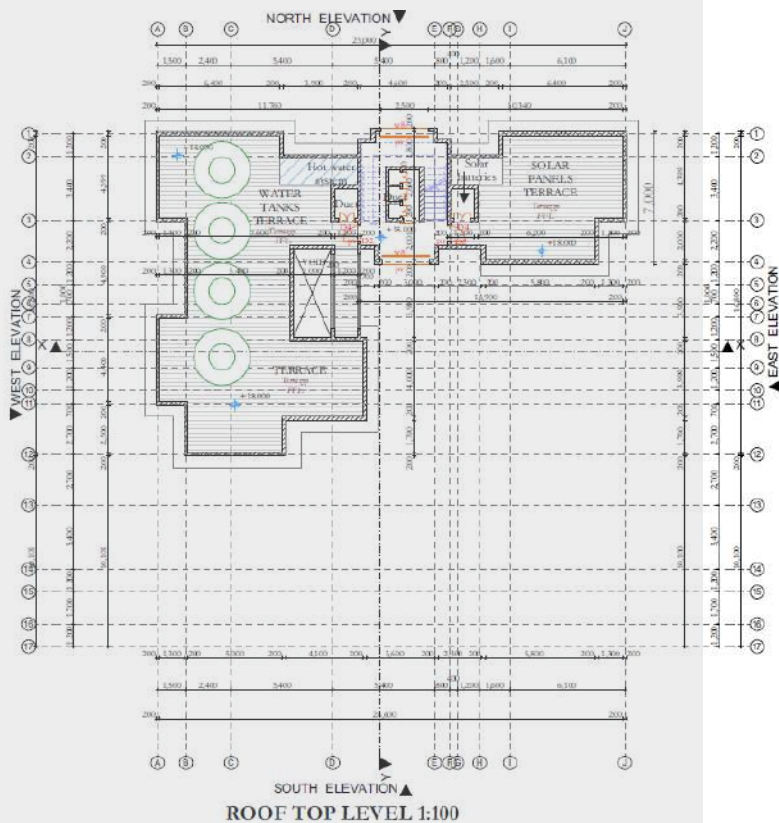

SITE PLAN 1:150

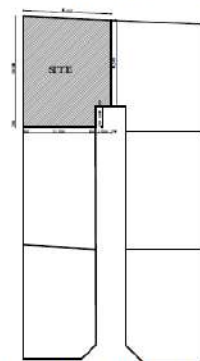

LOCATION PLAN 1:100

This space epitomizes architectural ingenuity, catering to the needs of individuals seeking a harmonious blend of style and functionality in their living spaces.

MODERN HOUSE IN KIKUYU

This modern-style maisonette in Kikuyu, Kiambu County, features five bedrooms with a focus on contemporary design and functionality.



The clean lines, expansive glass windows, and minimalist color palette create a harmonious connection with the natural surroundings. The open floor plan, equipped with a modern kitchen, promotes a communal atmosphere.



4-BEDROOM RUIRU.

4-bedroom modern style maisonette that seamlessly blends architectural innovation with comfort.

This masterpiece boasts clean lines, expansive windows, and a sleek façade that welcomes natural light into every corner. The open-plan layout creates a sense of fluidity, connecting the living spaces effortlessly.

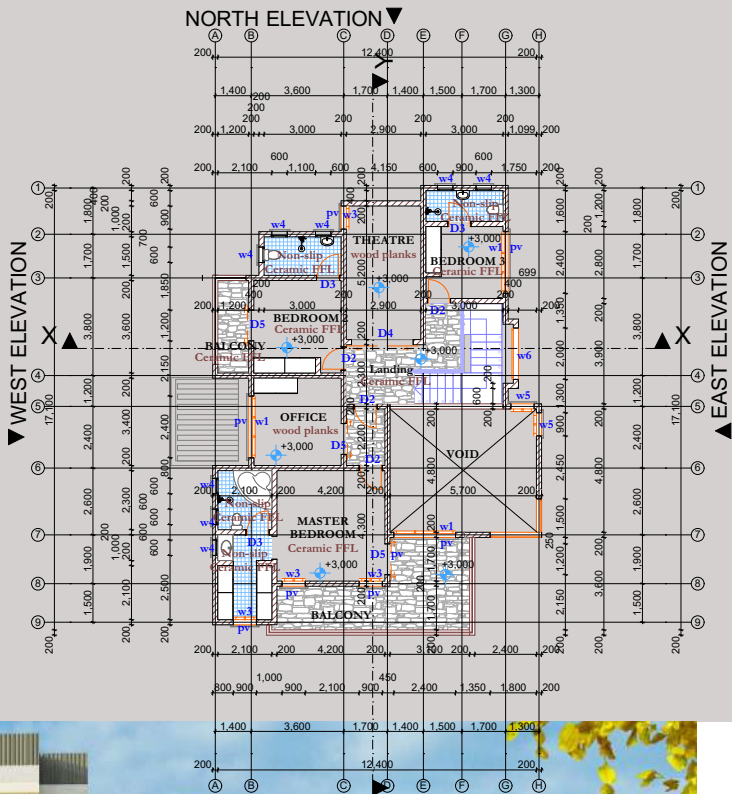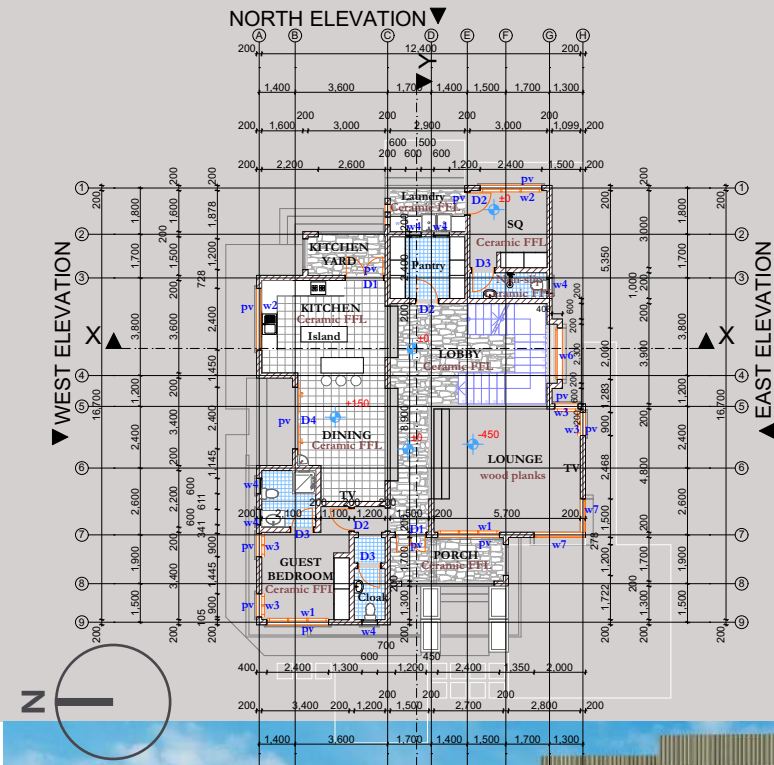




LANDSCAPING PROJECT IN LAVINGTON

In crafting the architectural design for the landscaping project in Lavington, Nairobi County, our primary goal is to seamlessly blend natural beauty with functional spaces, creating an environment that harmoniously integrates with the surrounding urban fabric.

The architectural elements, from carefully selected materials for hardscaping to artistic installations, reflect a commitment to aesthetic coherence and durability.

PROPOSED SITE

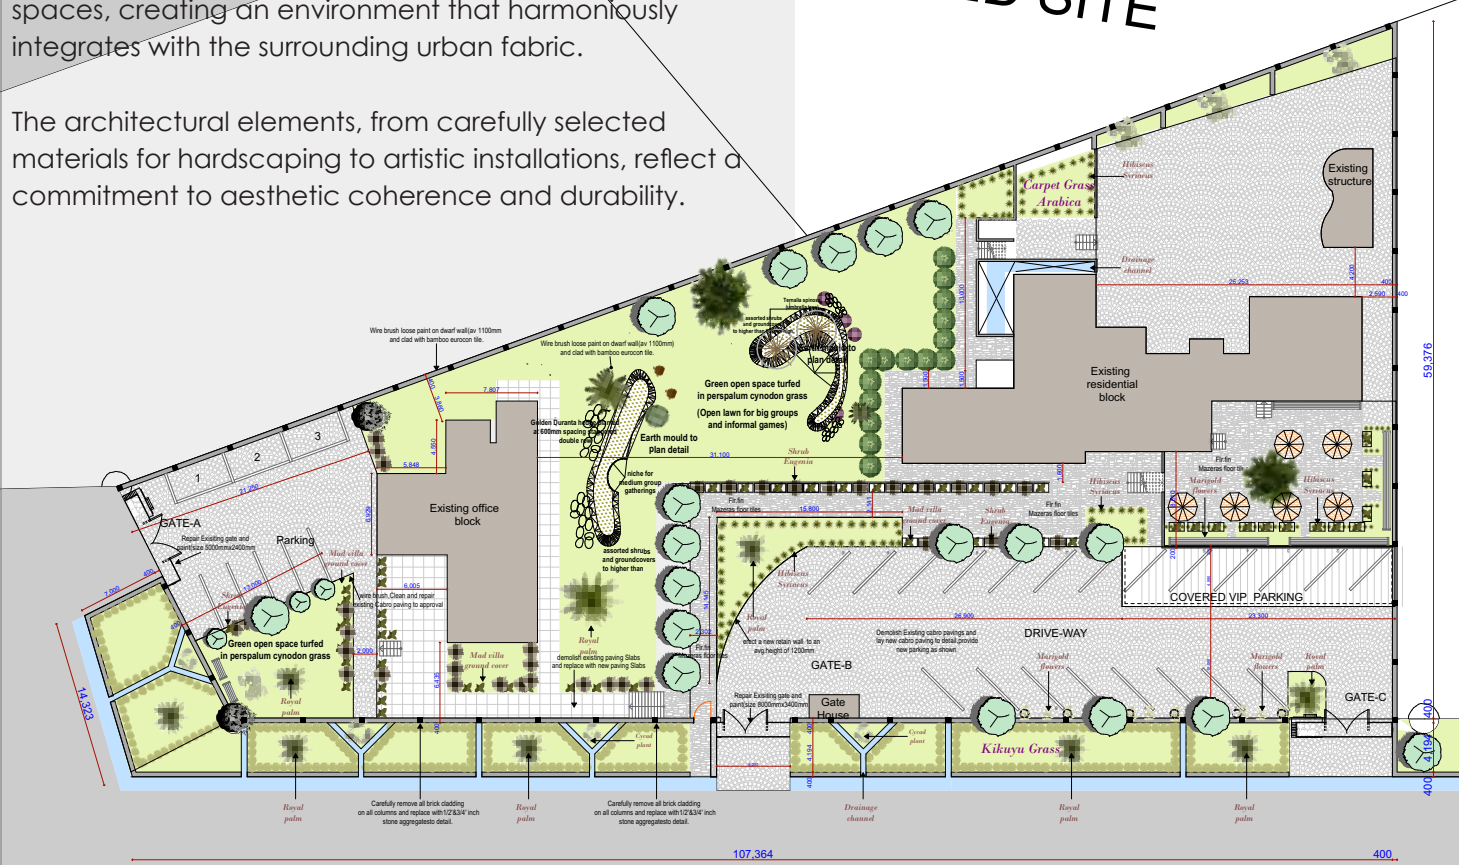

Masterplan











NGOIGWA THIKA APARTMENTS

Nested in the heart of Thika, Kenya, this residential development seamlessly integrates modern living with the rich cultural and environmental context of its surroundings.

The layout maximizes natural light and ventilation, promoting energy efficiency and a connection to the outdoors.

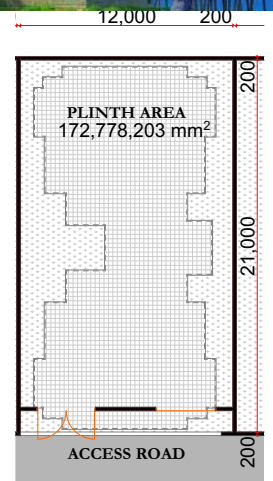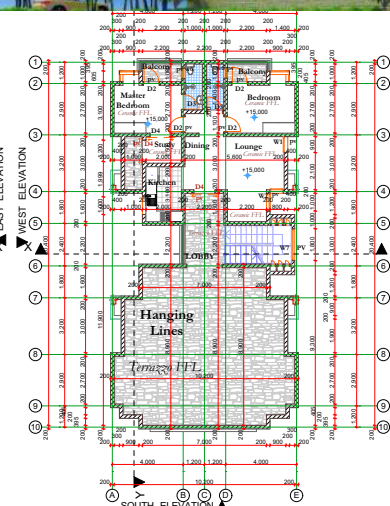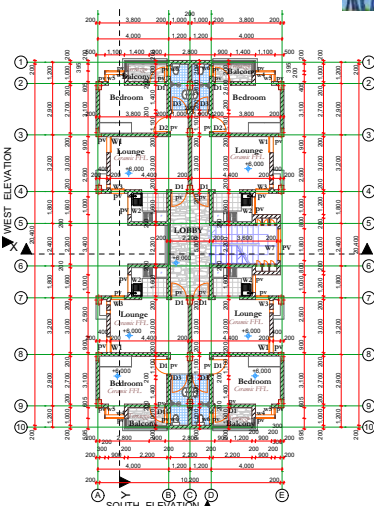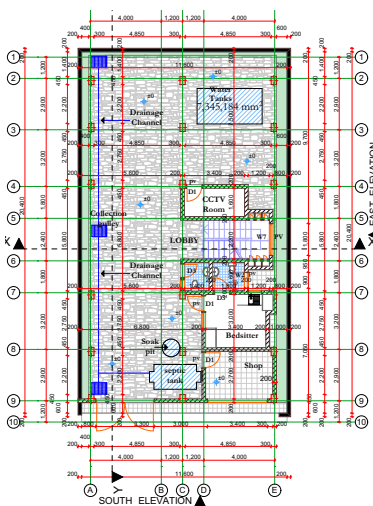

SITE PLAN 1:100



4 BEDROOM DUPLEXES- KAREN



Ground Floor plan



First Floor plan





WE-GO GROUP INTERIORS.

The interior design for the WE-GO Group in Kisii Town encapsulates a harmonious blend of functionality, aesthetics, and corporate identity.

Thoughtful space planning optimizes workflow efficiency while providing a comfortable and inspiring atmosphere for employees.

The color scheme and furniture selections align with the brand's vision, creating a cohesive and branded interior.



WE-GO GROUP INTERIORS.

The interior design for the WE-GO Group in Kisii Town encapsulates a harmonious blend of functionality, aesthetics, and corporate identity.

Thoughtful space planning optimizes workflow efficiency while providing a comfortable and inspiring atmosphere for employees.

The color scheme and furniture selections align with the brand's vision, creating a cohesive and branded interior.



WE-GO GROUP INTERIORS.

The interior design for the WE-GO Group in Kisii Town encapsulates a harmonious blend of functionality, aesthetics, and corporate identity.

Thoughtful space planning optimizes workflow efficiency while providing a comfortable and inspiring atmosphere for employees.

The color scheme and furniture selections align with the brand's vision, creating a cohesive and branded interior.




WE-GO GROUP INTERIORS.


The interior design for the WE-GO Group in Kisii Town encapsulates a harmonious blend of functionality, aesthetics, and corporate identity.

Thoughtful space planning optimizes workflow efficiency while providing a comfortable and inspiring atmosphere for employees.

The color scheme and furniture selections align with the brand's vision, creating a cohesive and branded interior.

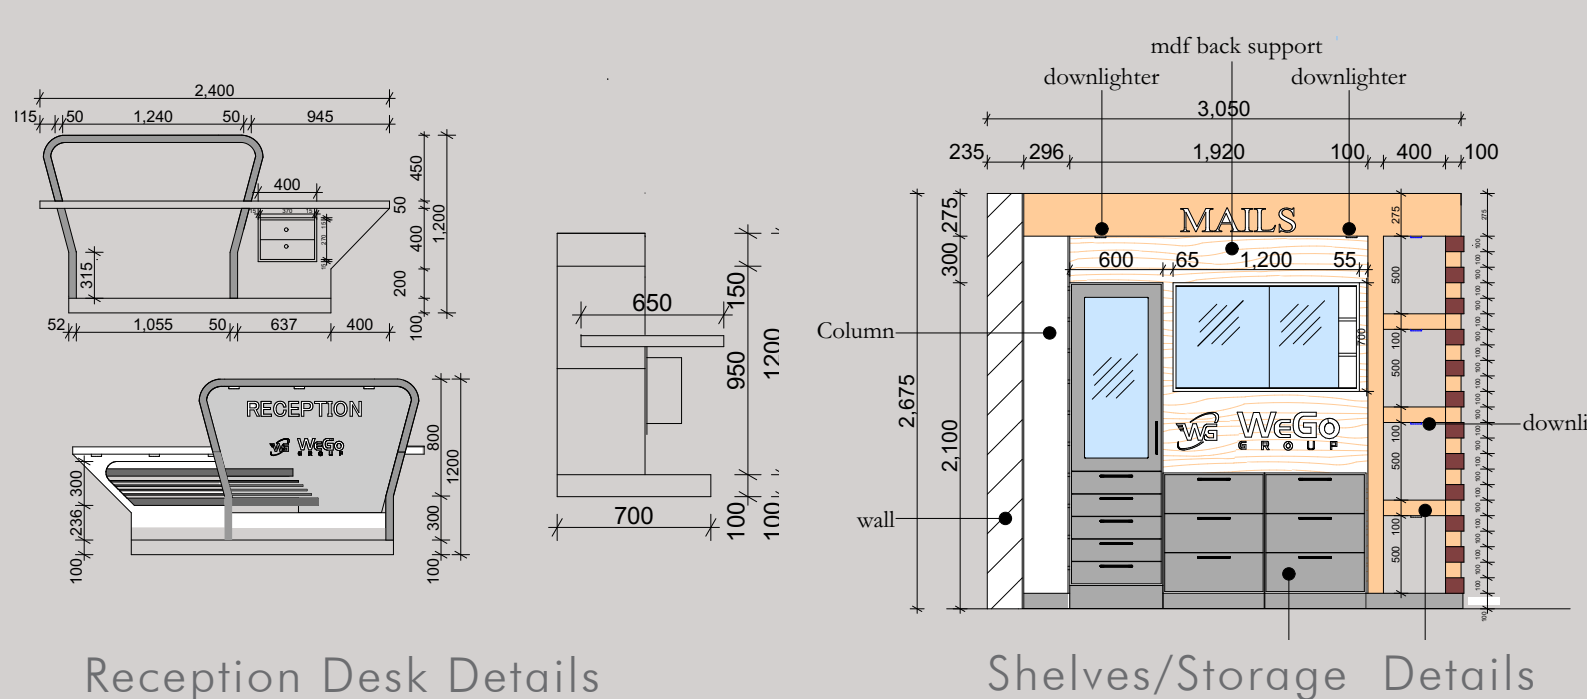

Reception Desk Details

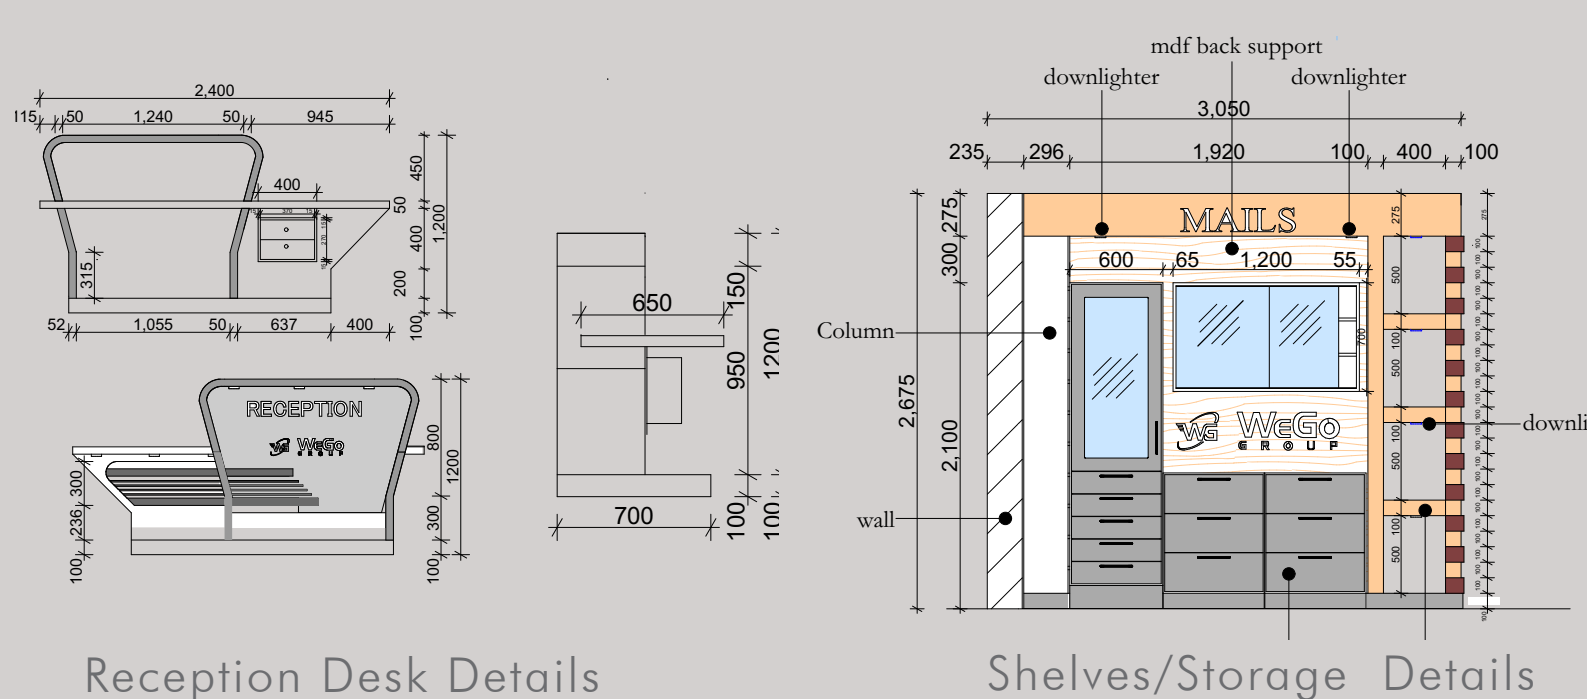

Shelves/Storage Details



ABUYA Z. NYAPENI.



THANK YOU..!

+254706179483/ +254789034630
abuyanyapeni@gmail.com

Copyright @ 2023